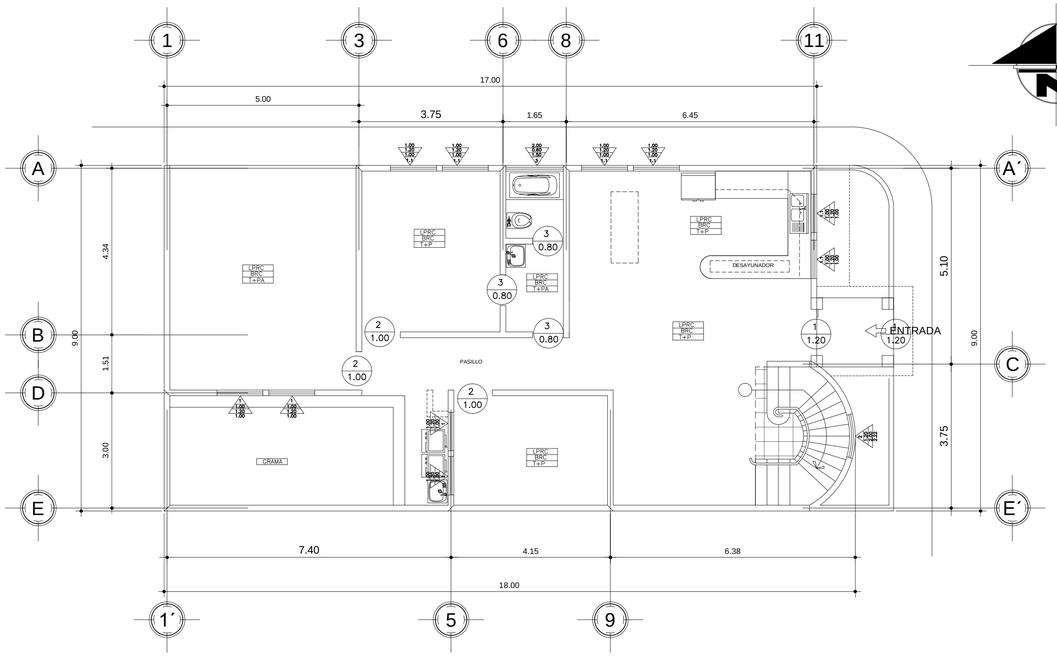

PLANTA DE ACABADOS NIVEL 1

VIVIENDA UNIFAMILIAR 2 NIVELES

ESCALA 1: 75

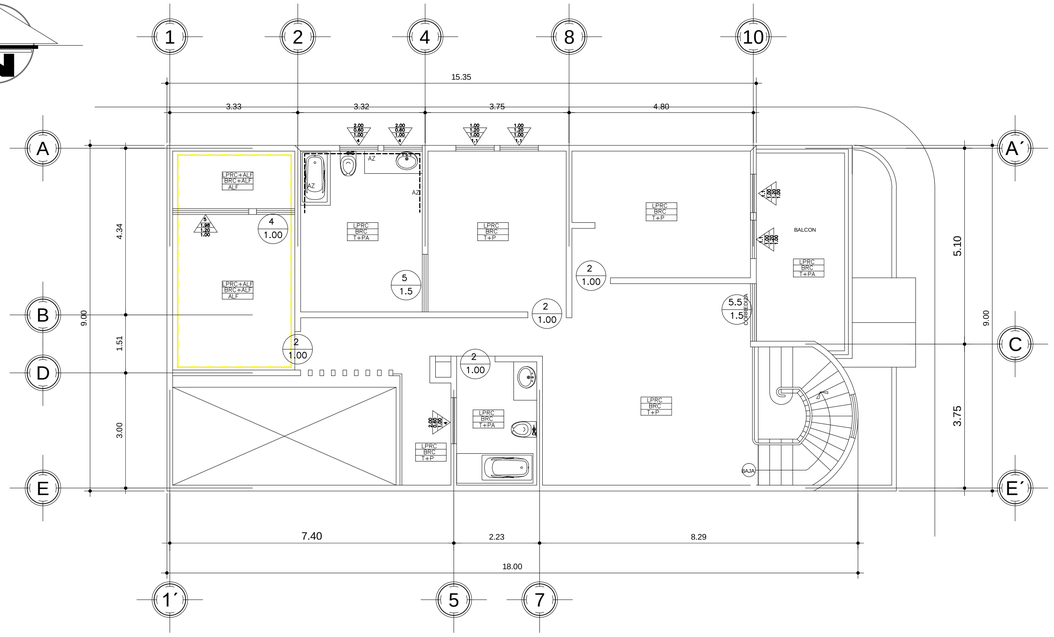

PLANTA DE ACABADOS NIVEL 2

VIVIENDA UNIFAMILIAR 2 NIVELES

ESCALA 1: 75

ELVEVACION FRONTAL

VIVIENDA UNIFAMILIAR 2 NIVELES

ESCALA 1: 75

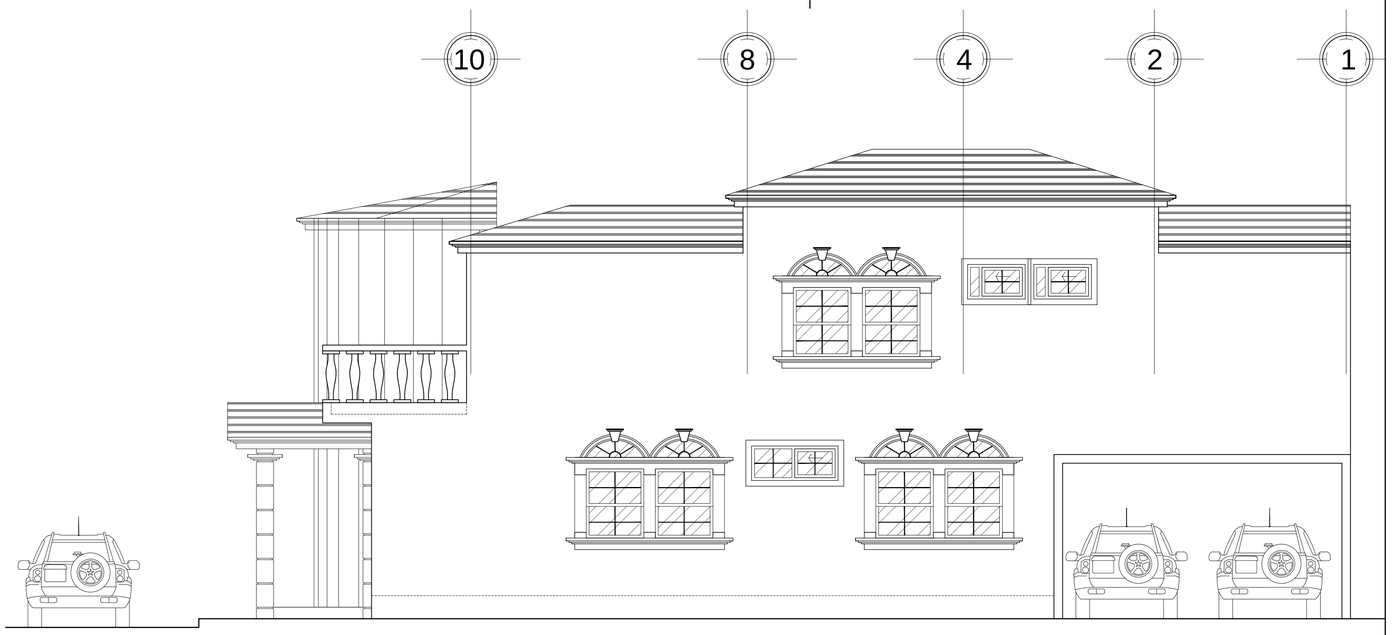

ELVEVACION LATERAL DERECHA

VIVIENDA UNIFAMILIAR 2 NIVELES

ESCALA 1: 75

NOTA:
VER DETALLES DE ACABADOS
EN HOJA No. 3

WD ARQUITECTURA

VIVIENDA UNIFAMILIAR
JUTIAPA, JUTIAPA

UNIDAD:
WD ARQUITECTURA

CONTENIDO:
PLANO DE ACABADOS + ELEVACIONES

ESCALA:
INDICADA
FECHA:
NOVIEMBRE 2021

DISEÑO:
WD ARQUITECTURA

DIBUJO:
WD ARQUITECTURA

CALCULO:
WD ARQUITECTURA

Vo.Bo.

PLANO DE:
A E I

HOJA No.
02/09