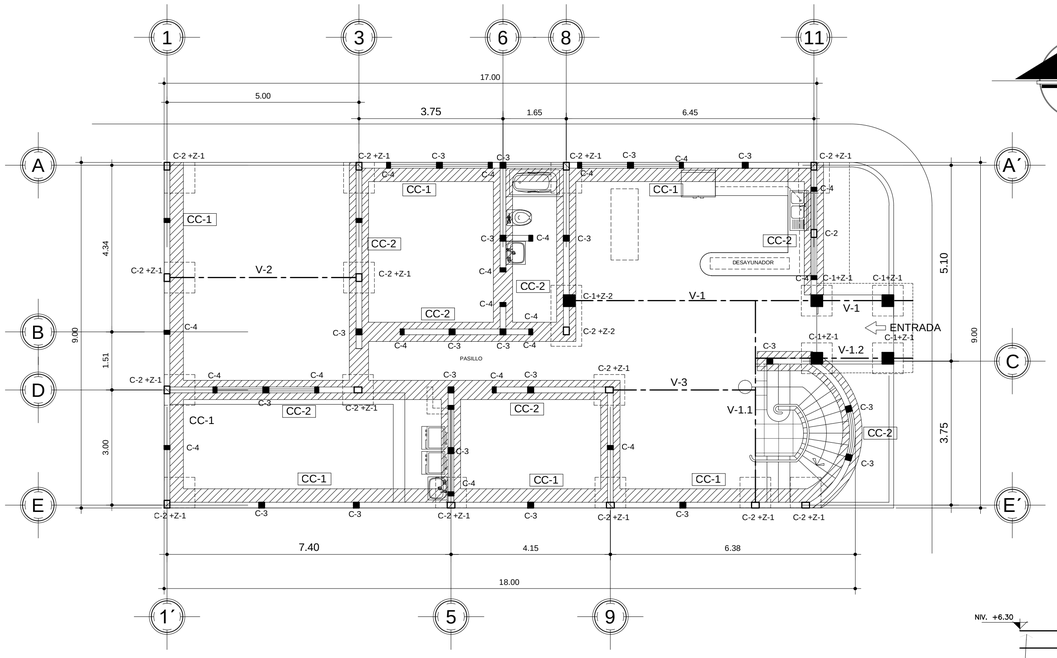

PLANTA DE CIMENTACION Y COLUMNAS NIVEL 1

VIVIENDA UNIFAMILIAR 2 NIVELES

ESCALA 1: 75

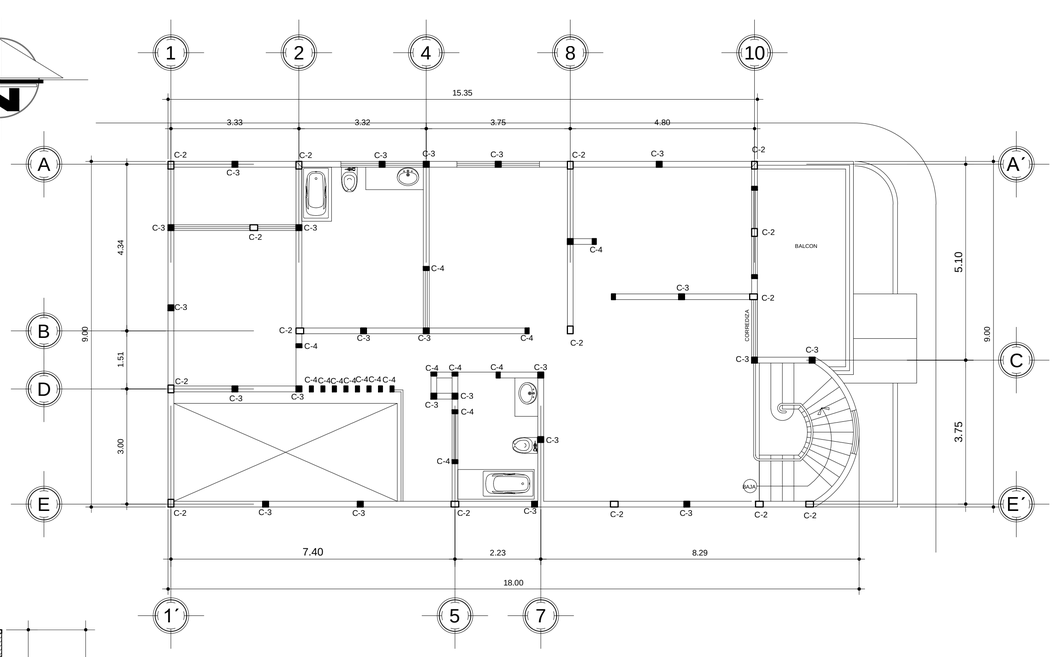

PLANTA DE CIMENTACION Y COLUMNAS NIVEL 2

VIVIENDA UNIFAMILIAR 2 NIVELES

ESCALA 1: 75

PLANILLA DE CIMIENTOS Y ZAPATAS

CIMIENTO TIPO	DIMENSIONES			REFUERZO LONGITUDINAL	ESTRIBOS Y/O ESLABONES
	LARGO	ANCHO	ALTO		
CC−1	VAR.	0.50	0.20	3 No.3	CIMIENTO CORRIDO/No.3 A CADA 0.15
CC−2	VAR.	0.50	0.20	3 No.3	CIMIENTO CORRIDO/No.3 A CADA 0.15
Z−1	0.80	0.80	0.20	No.4 @ 0.15 EN AMBOS SENTIDOS	ZAPATA TIPO Z−1/AMBOS SENTIDOS
Z−2	1.60	0.80	0.20	No.4 @ 0.15 EN AMBOS SENTIDOS	ZAPATA TIPO Z−2/AMBOS SENTIDOS
SH	VAR.	0.15	0.20	4 No.3	SOLERA HIDROFUGA/No.2 A CADA 0.15
SOL. I	VAR.	0.15	0.20	4 No.3	SOLERA INTEMEDIA/No.2 A CADA 0.15

PLANILLA DE COLUMNAS

NOMENCLATURA		DIMENSIONES		REFUERZO LONGITUDINAL	ESTRIBOS Y/O ESLABONES	DETALLES SIN ESCALA
COLUMNA	TIPO	ANCHO	LARGO			
C1		0.30	0.30	4 No.4 4 No.3	EST. No.2 A CADA 0.15	
C2		0.15	0.20	4 No.4	EST. No.2 A CADA 0.15	
C3		0.15	0.15	4 No.3	EST. No.2 A CADA 0.15	
C4		0.10	0.15	2 No.3	ESL. No.2 A CADA 0.15	
CONCRETO	USO: CIMIENTO, COLUMNAS, VIGAS SOLERAS Y LOSAS				F´c = 210 kg/ cm2. 3,000 PSI	
ACERO	USO: CIMIENTO, COLUMNAS, VIGAS SOLERAS Y LOSAS				F´y = 2810 kg/ cm2. 40,000 PSI	

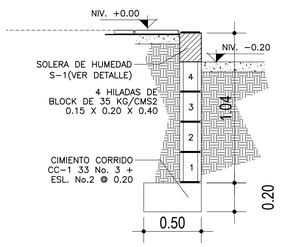

CIMIENTO CORRIDO CC-1

SECCION ESCALA 1:20

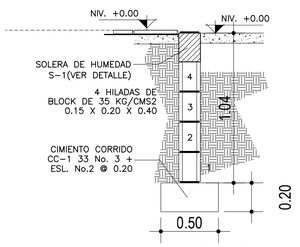

CIMIENTO CORRIDO CC-2

SECCION ESCALA 1:20

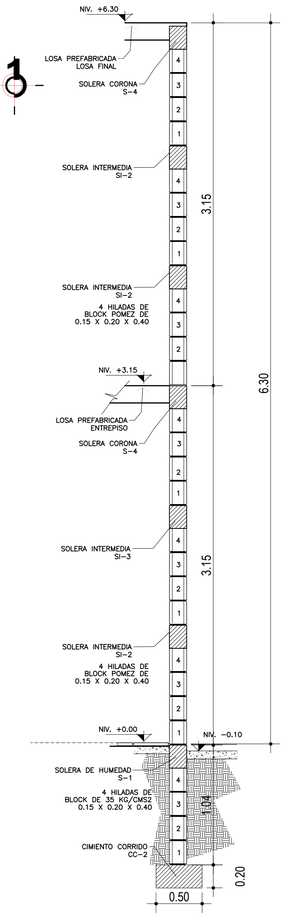

SECCION TIPICA MURO

MURO DE CONTENCION ESCALA 1:25

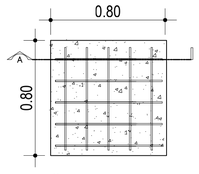

ZAPATA Z-1

PLANTA ESCALA 1:20

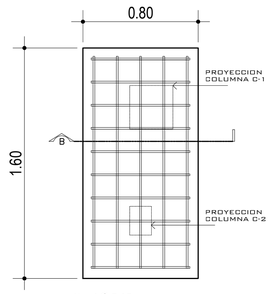

ZAPATA Z-2

PLANTA ESCALA 1:20

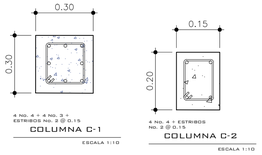

COLUMNA C-1

ESCALA 1:10

COLUMNA C-2

ESCALA 1:10

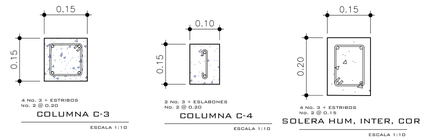

COLUMNA C-3

ESCALA 1:10

COLUMNA C-4

ESCALA 1:10

SOLERA HUM. INTER. COR

ESCALA 1:10

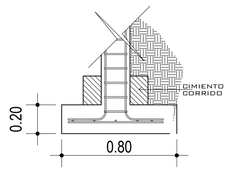

ZAPATA Z-1

SECCION A ESCALA 1:20

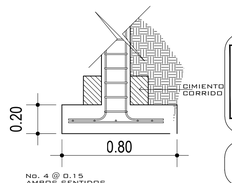

ZAPATA Z-2

SECCION B ESCALA 1:20

VIVIENDA UNIFAMILIAR
JUTIAPA, JUTIAPA

UNIDAD:
WD ARQUITECTURA

CONTENIDO:
PLANO DE CIMENTACION Y COLUMNAS

ESCALA: INDICADA
FECHA: NOVIEMBRE 2021

DISEÑO: WD ARQUITECTURA
DIBUJO: WD ARQUITECTURA
CALCULO: WD ARQUITECTURA

Vo.Bo.

PLANO DE: A E I

HOJA No. 04/09