VER DETALLES DE PUERTAS Y VENTANAS EN PLANO DE DETALLES ANEXOS

NOMENCLATURA DE ACABADOS

Ventaneria
- TIPO #
- ANCHO
- ALTO
- ALTURA DE SILLAR

ACABADO EN CUBIERTA
ACABADO EN PARED
ACABADO EN PISO

Puertas
- TIPO #
- ANCHO

NOMENCLATURA	DESCRIPCIÓN
LPRC	LOSA PREFABRICADA CON ESPESOR DE 0.7 CM DE RECUBRIMIENTO DE CONCRETO + REPELLO + CERNIDO.
BRC	BLOCK + 1 CAPA DE MONOCAPA GRIS + 1 CAPA DE MONOCAPA BLANCO
T+P	TORTA DE CONCRETO ESPESOR DE 0.05 M + PISO PORCELANATO
T+PA	TORTA DE CONCRETO ESPESOR DE 0.08 M + PISO ANTIDESLIZANTE
BC	BANQUETAS FUNDICION DE CONCRETO DE 0.10 CENTIMETROS.
AZ	AZULEJO EN PARED COLOR INDICADO POR EL SUPERVISOR MUNICIPAL ALTURA 1.50 METROS
ALF	RECUBRIMIENTO DE ALFOMBRA –SISTEMA ACUSTICO–

PLANILLA DE VENTANAS

TIPO	CANTIDAD	ALTO	ANCHO	SILLAR	DESCRIPCION	UBICACIÓN
V-1	4	1.20	1.00	1.00	PVC + VIDRIO	SALA, COCINA, CUARTOS GARAGE
V-1.1	10	1.20	1.00	1.00	PVC + VIDRIO	SALA, COCINA, CUARTOS GARAGE
V-2	1	2.00	1.2	2.22	PVC + VIDRIO	MODULO DE GRADAS
V-3	1	0.60	1.50	2.00	PVC + VIDRIO	SERVICIO SANITARIO NIVEL 1
V-4	3	0.60	1.00	2.00	PVC + VIDRIO	SERVICIOS SANITARIOS NIVEL 2
V-5	1	1.20	1.98	1.00	PVC + VIDRIO	CABINA DE AUDIO

PLANILLA DE PUERTAS

TIPO	CANTIDAD	DINTEL	ANCHO	OBSERVACIONES	UBICACION
P-1	02	2.40	1.20	MADERA	INGRESO PRINCIPAL
P-2	07	2.40	1.00	MADERA ENCHAPADA	HABITACIONES, GARAGE, ESTUDIO S.S COMPARTIDO NIVEL 2
P-3	03	2.40	0.80	MADERA ENCHAPADA	S.S COMPARTIDO NIVEL 1
P-4	01	2.40	1.00	PVC + VIDRIO TRASLUCIDO HERMETICO	ESTUDIO
P-5	01	2.40	1.50	PVC + VIDRIO CORREDIZO	S.S HABITACION PRINCIPAL
P-6	01	2.40	1.50	PVC + VIDRIO CORREDIZO	BALCON

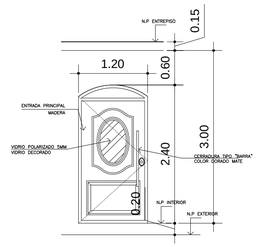

PUERTA TIPO 1
ENTRADA PRINCIPAL ESCALA 1:50

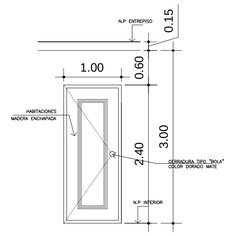

PUERTA TIPO 2
HABITACIONES ESCALA 1:50

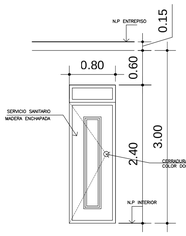

PUERTA TIPO 3
SERVICIO SANITARIO ESCALA 1:50

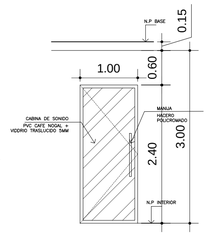

PUERTA TIPO 4
CABINA DE SONIDO ESCALA 1:50

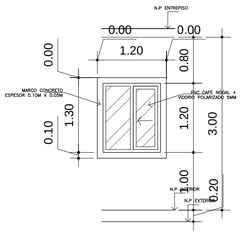

VENTANA TIPO 1
ESCALA 1:50

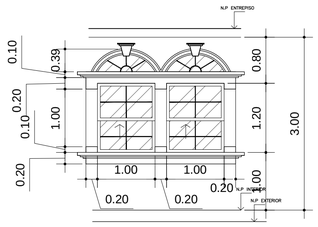

VENTANA TIPO 1.1
ESCALA 1:50

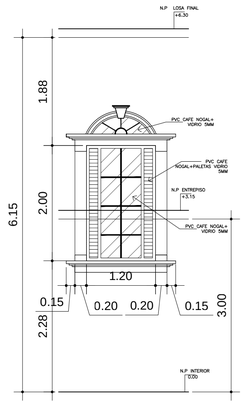

VENTANA TIPO 2
ESCALA 1:50

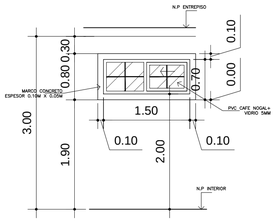

VENTANA TIPO 3
ESCALA 1:50

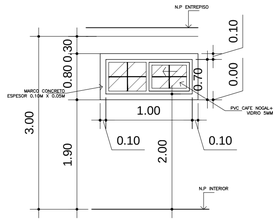

VENTANA TIPO 4
ESCALA 1:50

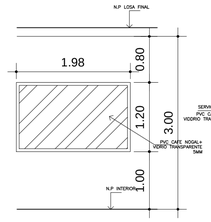

VENTANA TIPO 5
ESCALA 1:50

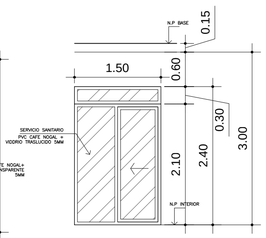

PUERTA TIPO 5
CABINA DE SONIDO ESCALA 1:50

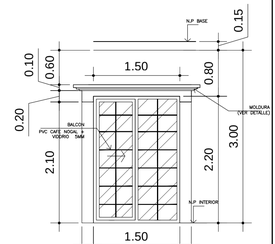

PUERTA TIPO 6
BALCON ESCALA 1:50

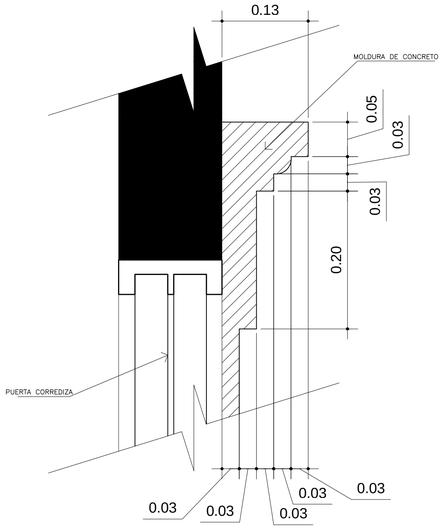

DETALLE MOLDURA VANO A BALCON
VIVIENDA UNIFAMILIAR 2 NIVELES ESCALA 1: SIN

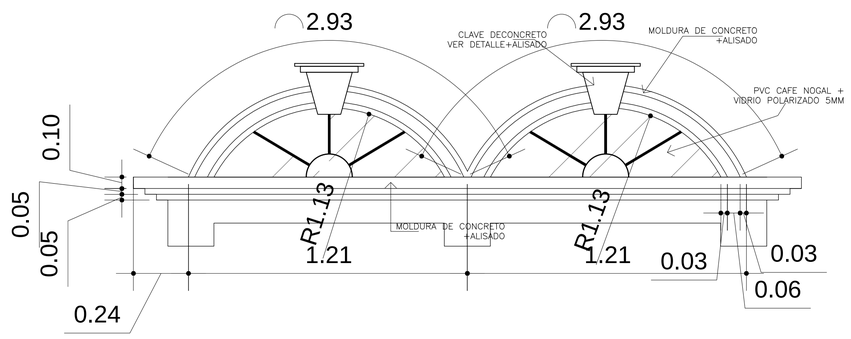

DETALLE MOLDURA EN ARCO
VIVIENDA UNIFAMILIAR 2 NIVELES ESCALA 1: 10

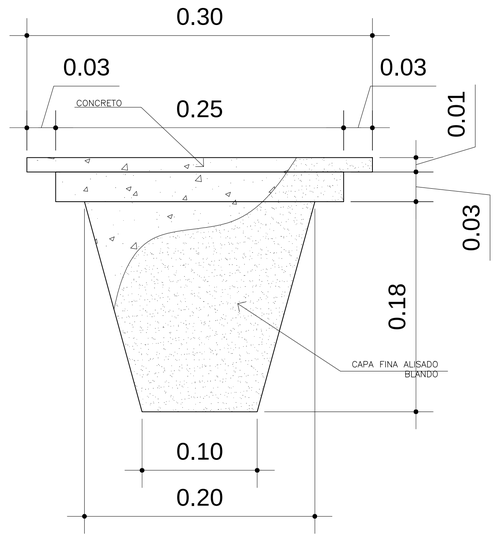

VIVIENDA UNIFAMILIAR
JUTIAPA, JUTIAPA

UNIDAD: WD ARQUITECTURA

CONTENIDO: PLANO DETALLES PUERTAS Y VENTANAS

ESCALA: INDICADA
FECHA: NOVIEMBRE 2021

DISEÑO: WD ARQUITECTURA
DIBUJO: WD ARQUITECTURA
CALCULO: WD ARQUITECTURA

Vo.Bo.

PLANO DE: A E I
HOJA No. 03/09