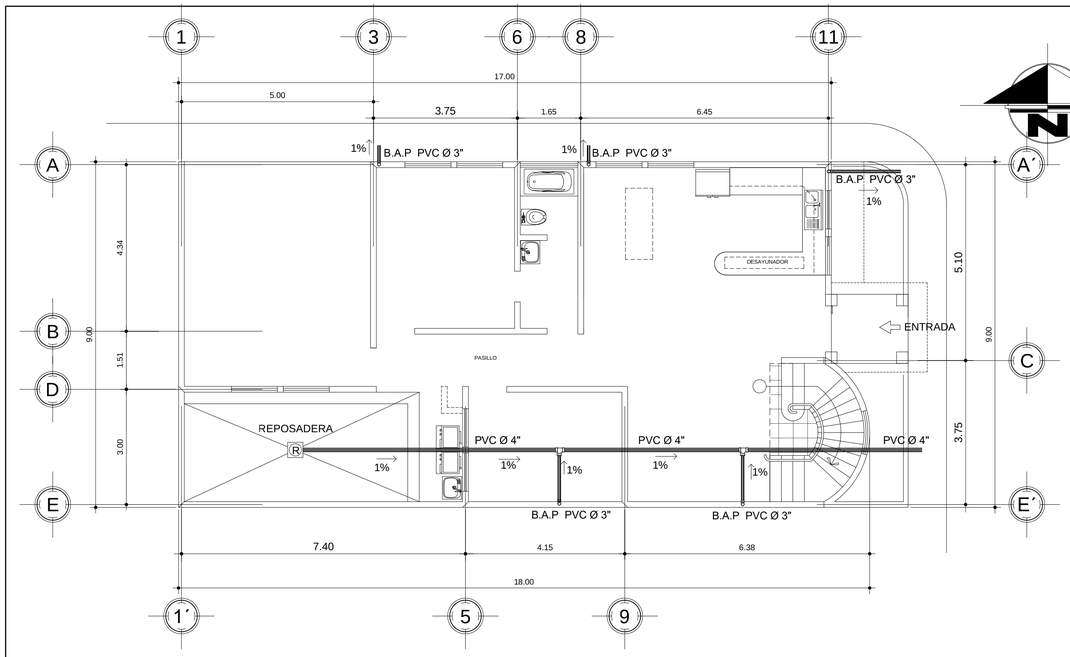

PLANTA DE INST. PLUVIAL NIVEL 1

VIVIENDA UNIFAMILIAR 2 NIVELES

ESCALA 1: 75

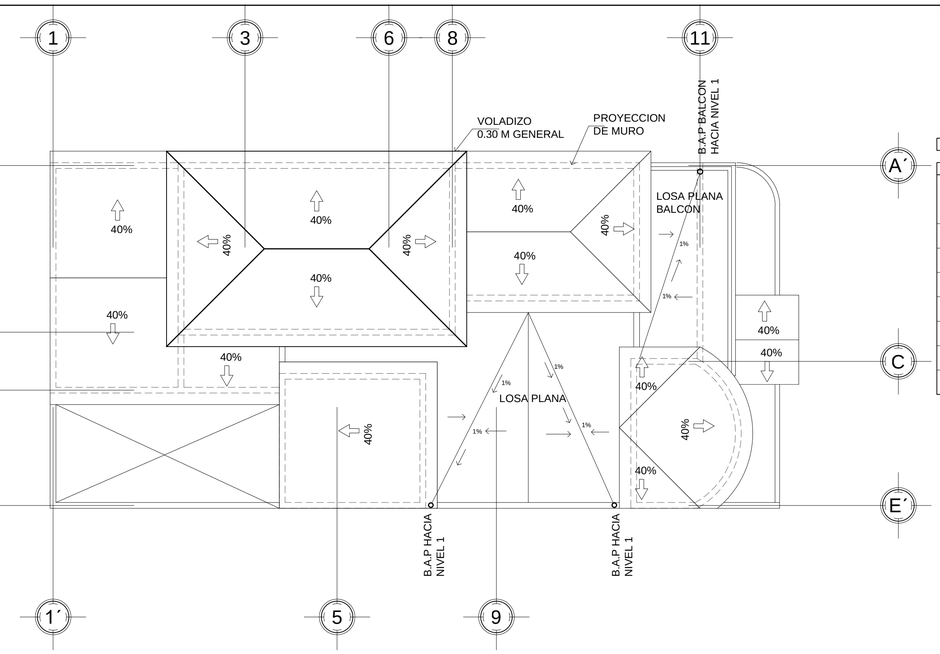

SIMBOLOGIA DE AGUA PLUVIAL	
SÍMBOLO	SIGNIFICADO
R	REPOSADERA EN JARDIN
	PENDIENTE DE TECHOS AGUA PLUVIAL
	TUBO DE DRANAJE AGUA PLUVIAL
	REDUCTOR
	TE PERFIL
	CODO 90° ELEVACIÓN
	BAJADA DE AGUA PLUVIAL

SIMBOLOGÍA DE ILUMINACIÓN	
SÍMBOLO	SIGNIFICADO
	CONTADOR h=2.40 S.N.P.T. (VER DETALLE EN HOJA No. 12)
	TABLERO DE DISTRIBUCIÓN h=1.70 S.N.P.T.
	TUBO PVC ELÉCTRICO ø 3/4" O INDICADO EN LOSA
	ILUMINACIÓN EN CIELO
	ILUMINACIÓN EN PARED h=2.00 S.N.P.T. (SI NO SE INDICA OTRO)
	REFLECTOR h=2.20 S.N.P.T.
	LÍNEA NEUTRAL CALIBRE 12 THN O INDICADO
	LÍNEA DE PUENTE CALIBRE 12 THN O INDICADO
	LÍNEA VIVA CALIBRE 12 THN O INDICADO
	LÍNEA DE RETORNO CALIBRE 14 THN O INDICADO
	INTERRUPTOR DOBLE CON DADO DE TOMACORRIENTE SOLO EN BAÑOS H=1.20 S.N.P.T.
	INTERRUPTOR SIMPLE H=1.10 S.N.P.T. (VER DETALLE EN HOJA No. 12)
	INTERRUPTOR DOBLE H=1.10 S.N.P.T. (VER DETALLE EN HOJA No. 12)

PLANTA DE TECHOS

VIVIENDA UNIFAMILIAR 2 NIVELES

ESCALA 1: 75

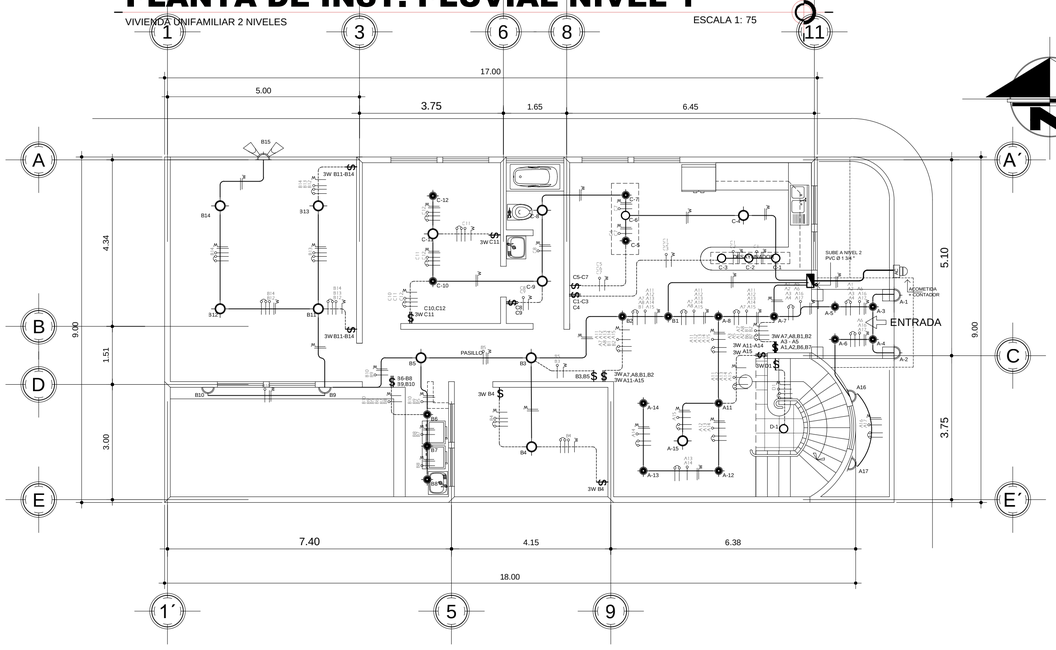

PLANTA DE INST. ELECTRICA-ILUMINACION NIVEL 1

VIVIENDA UNIFAMILIAR 2 NIVELES

ESCALA 1: 75

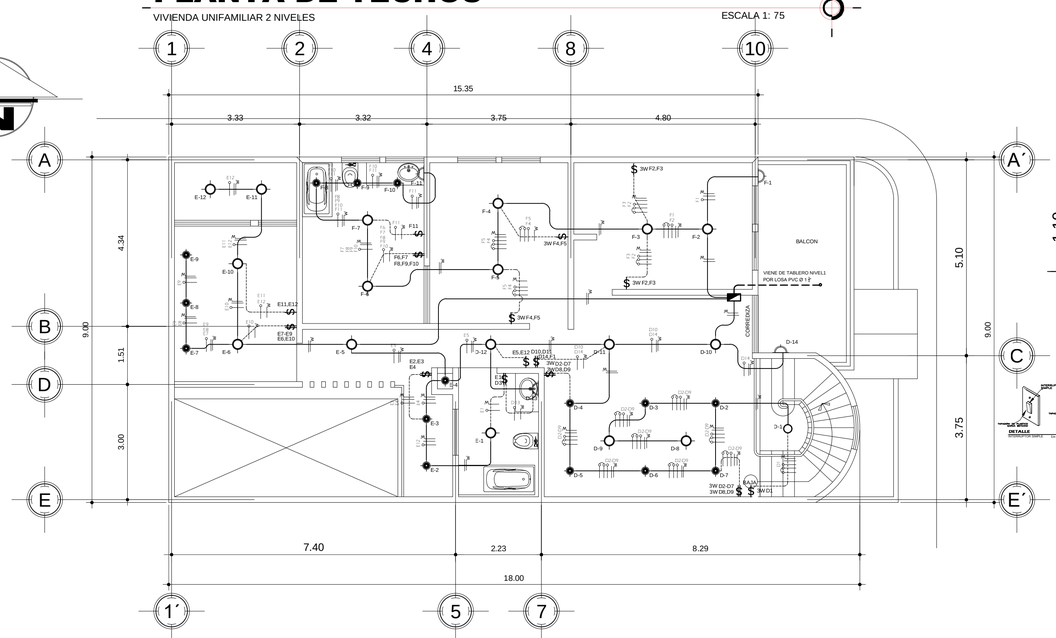

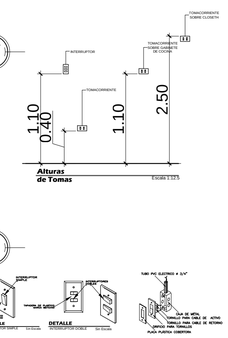

PLANTA DE INST. ELECTRICA-ILUMINACION NIVEL 2

VIVIENDA UNIFAMILIAR 2 NIVELES

ESCALA 1: 75

VIVIENDA UNIFAMILIAR
JUTIAPA, JUTIAPA

UNIDAD:
WD ARQUITECTURA

CONTENIDO:
PLANO DE INST. PLUVIAL + INST. ELECTRICAS- ILUMINACION

ESCALA:
INDICADA

FECHA:
NOVIEMBRE 2021

DISEÑO:
WD ARQUITECTURA

DIBUJO:
WD ARQUITECTURA

CALCULO:
WD ARQUITECTURA

Vo.Bo.

PLANO DE:
A | E | I

HOJA No.
08/09