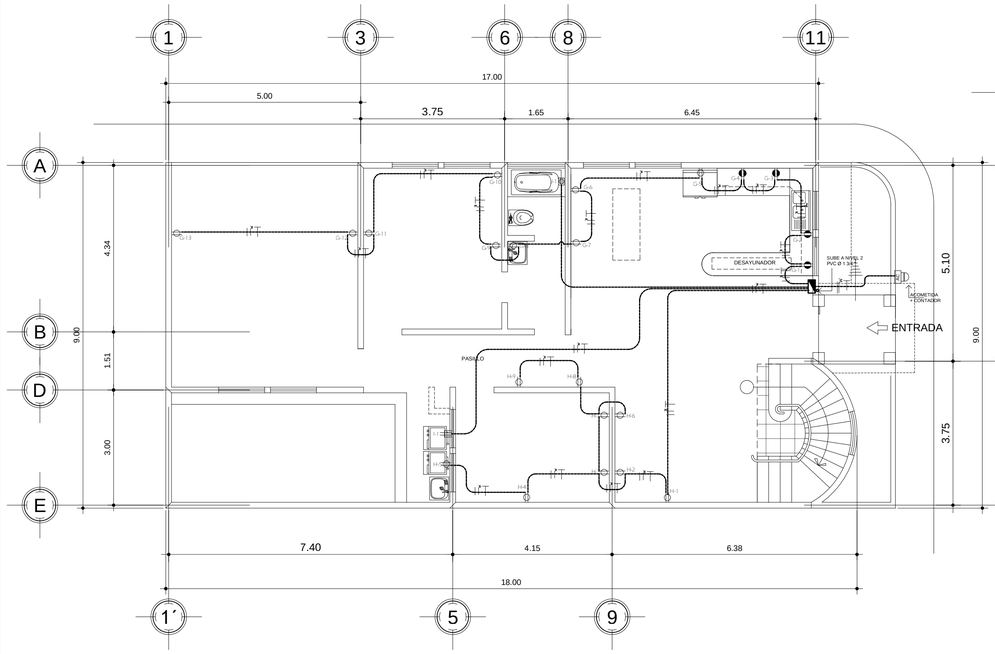

PLANTA DE INST. ELECTRICA-FUERZA NIVEL 1

VIVIENDA UNIFAMILIAR 2 NIVELES

ESCALA 1: 75

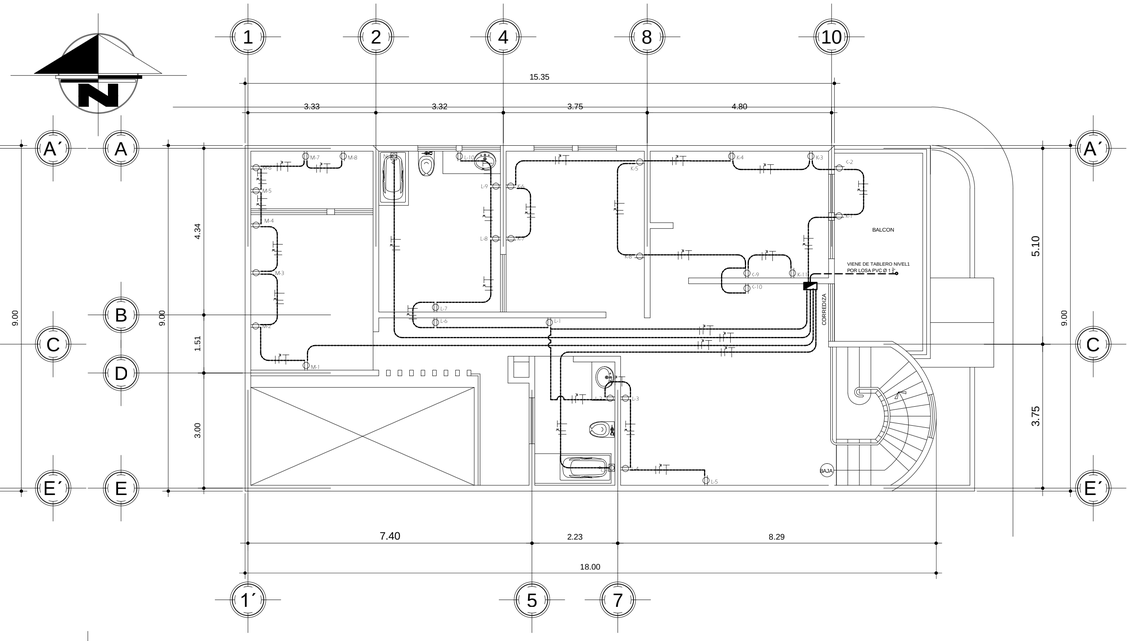

PLANTA DE INST. ELECTRICA-FUERZA NIVEL 2

VIVIENDA UNIFAMILIAR 2 NIVELES

ESCALA 1: 75

SIMBOLOGÍA DE FUERZA	
SÍMBOLO	SIGNIFICADO
	LINEA NEUTRAL CALIBRE 12 TW O INDICADO
	LINEA VIVA CALIBRE 12 TW O INDICADO
	LINEA DE TIERRA CALIBRE 12 TW O INDICADO
	TUBO PVC ELÉCTRICO ø 3/4" O INDICADO BAJO TIERRA
	TOMACORRIENTE SIMPLE 220 V. h=0.40 S.N.P.T.
	TOMACORRIENTE DOBLE 110 V. h=0.40 S.N.P.T. (VER DETALLE EN HOJA No. 12)
	TOMACORRIENTE DOBLE 110 V. h=1.10 S.N.P.T. SI NO SE INDICA LO CONTRARIO (VER DETALLE EN HOJA No. 12)
	INTERRUPTOR DOBLE CON DADO DE TOMACORRIENTE SOLO EN BAÑOS H=1.20 S.N.P.T.
	TOMACORRIENTE SIMPLE 220 V. (SOLO EN DUCHA) H=2.30 S.N.P.T.
	TIERRA FISICA VARILLA DE COBRE DE 5/8"
	CONTADOR h=2.40 S.N.P.T. (VER DETALLE EN HOJA No. 12)
	TABLERO DE DISTRIBUCIÓN ELECTRICO h=1.70 S.N.P.T.

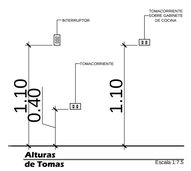

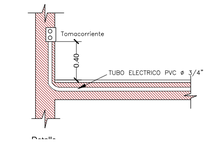

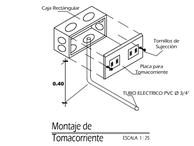

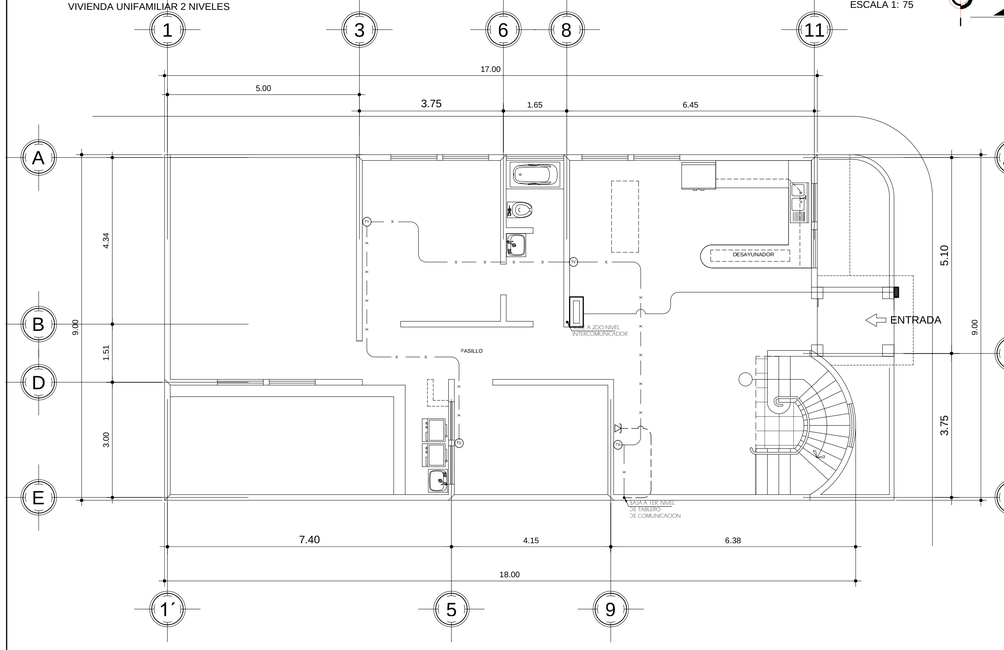

PLANTA DE INSTALACIONES ESPECIALES NIVEL 1

VIVIENDA UNIFAMILIAR 2 NIVELES

ESCALA 1: 75

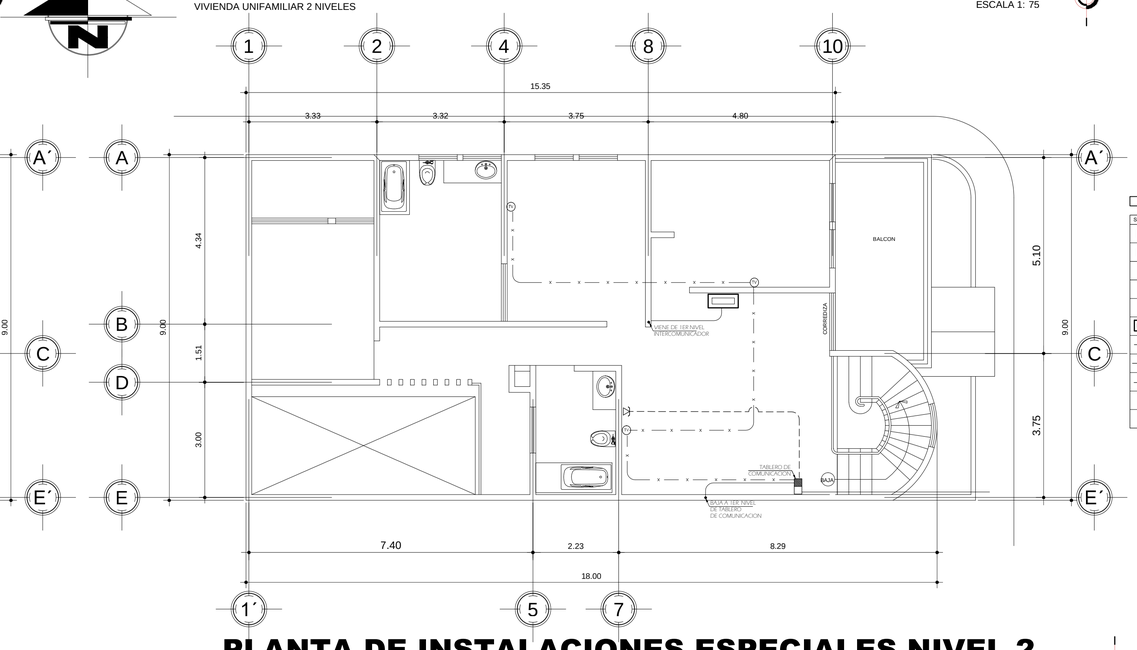

PLANTA DE INSTALACIONES ESPECIALES NIVEL 2

VIVIENDA UNIFAMILIAR 2 NIVELES

ESCALA 1: 75

SIMBOLOGÍA	
SÍMBOLO	SIGNIFICADO
	TABLERO DE DISTRIBUCIÓN ELECTRICO h=1.70 mts S.N.P.T.
	TABLERO DE DISTRIBUCIÓN DE COMUNICACION h=5.70 mts (SOBRE LOSA)
	SALIDA PARA INTERNET LAND h=0.40 mts S.N.P.T.
	SALIDA PARA TELEVISION POR CABLE h=0.40 mts S.N.P.T.
	TIMBRE h=1.70 mts S.N.P.T.
	SALIDA PARA PANTALLA DE TIMBRE, EN CAJA RECTANGULAR METALICA DE 4" X 2" CON ACCESORIO DE PRIMERA CALIDAD, h=2.20 mts S.N.P.T.
— X —	TUBERIA PARA CABLE TV EN PISO, PVC ELECTRICO ø 3/4", EXCEPTO SI INDICA OTRA
	FUBERIA PARA TELEFNO E INTERCOMUNICADOR EN PISO, PVC ELECTRICO ø 3/4", EXCEPTO SI INDICA OTRA
	TUBERIA PARA TIMBRE ø 3/4", EXCEPTO SI INDICA OTRA

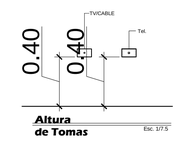

VIVIENDA UNIFAMILIAR
JUTIAPA, JUTIAPA

UNIDAD:
WD ARQUITECTURA

CONTENIDO:
PLANO DE INST. ELECTRICAS- FUERZA + INSTALACIONES ESPECIALES

ESCALA: INDICADA
FECHA: NOVIEMBRE 2021

DISEÑO: WD ARQUITECTURA
DIBUJO: WD ARQUITECTURA
CALCULO: WD ARQUITECTURA

Vo.Bo.

PLANO DE: A E I
HOJA No. 09/09