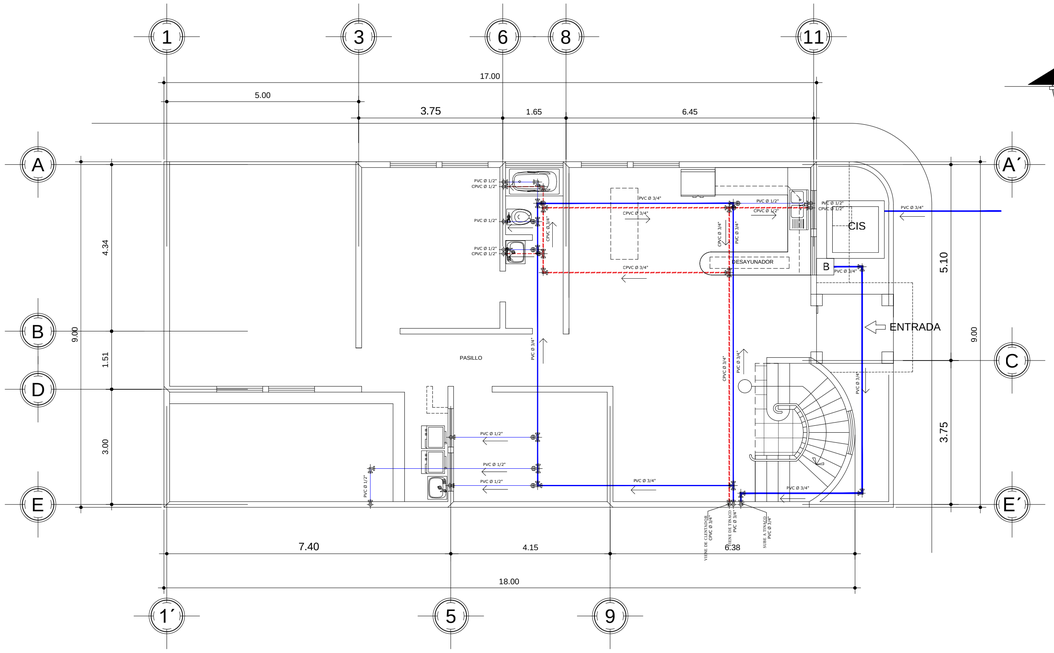

PLANTA DE INST. HIDRAULICA NIVEL 1

VIVIENDA UNIFAMILIAR 2 NIVELES

ESCALA 1: 75

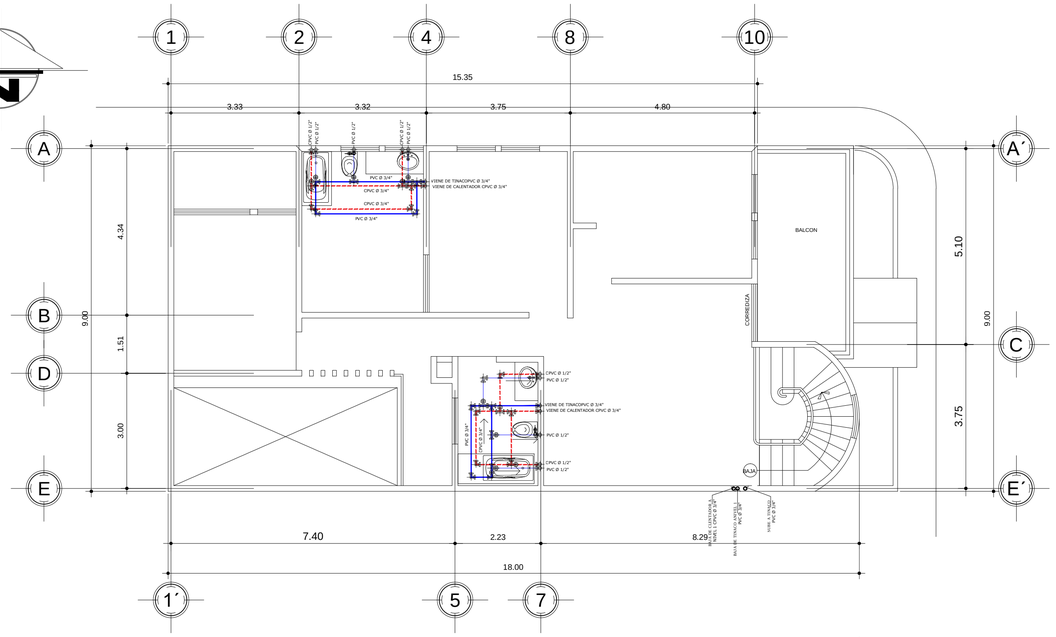

PLANTA DE INST. HIDRAULICA NIVEL 2

VIVIENDA UNIFAMILIAR 2 NIVELES

ESCALA 1: 75

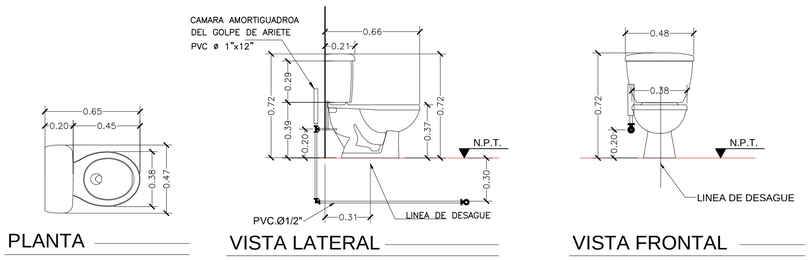

DETALLE DE INODORO

STANDARD"

ESCALA 1/20

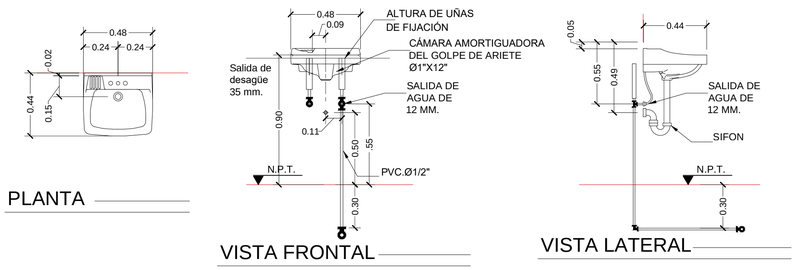

DETALLE DE LAVAMANOS

ESCALA 1/20

SIMBOLOGIA

	CODO PVC A 90°
	CODO PVC A 90°
	TEE PVC
	REDUCIDOR
TUBERIA PVC	TUBERIA PVC DE AGUA POTABLE, Ø INDICADO
TUBERIA CPVC	TUBERIA CPVC DE AGUA CALIENTE Ø INDICADO

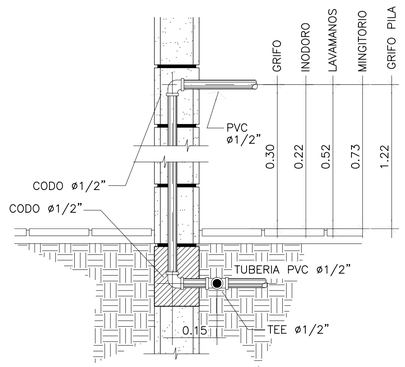

DETALLE

DETALLE DE TOMA DE AGUA PARA ARTEFACTOS SANITARIOS

ESCALA 1:20

VIVIENDA UNIFAMILIAR
JUTIAPA, JUTIAPA

UNIDAD: WD ARQUITECTURA

CONTENIDO: PLANO DE INST. HIDRAULICA + DETALLES

ESCALA: INDICADA

FECHA: NOVIEMBRE 2021

DISEÑO: WD ARQUITECTURA

DIBUJO: WD ARQUITECTURA

CALCULO: WD ARQUITECTURA

Vo.Bo.

PLANO DE: A E I

HOJA No. 06/09