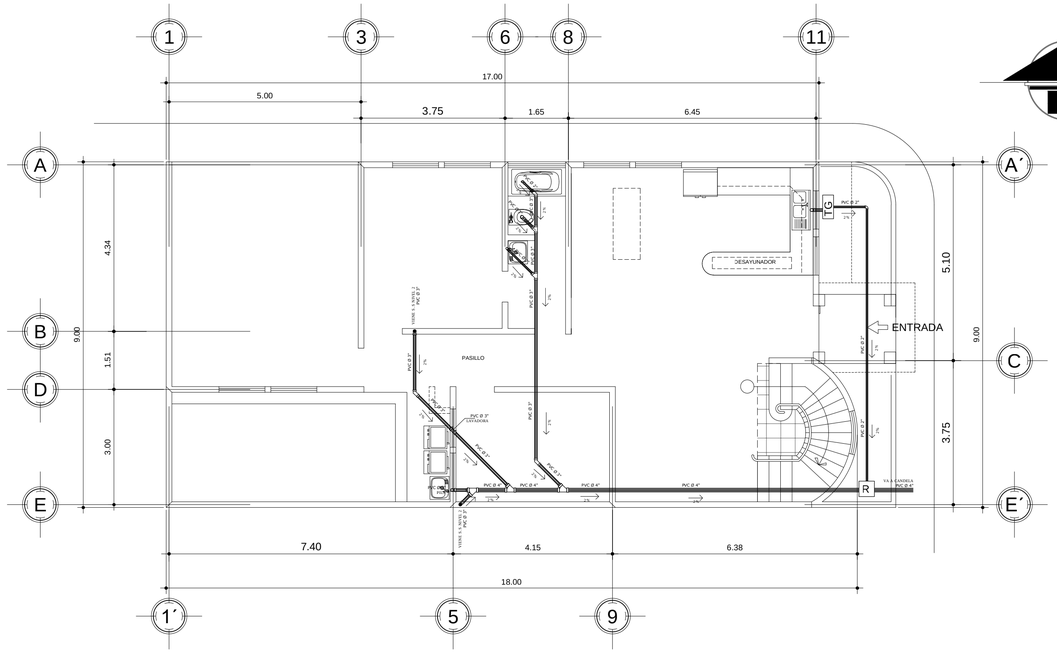

PLANTA DE INST. SANITARIA NIVEL 1

VIVIENDA UNIFAMILIAR 2 NIVELES

ESCALA 1: 75

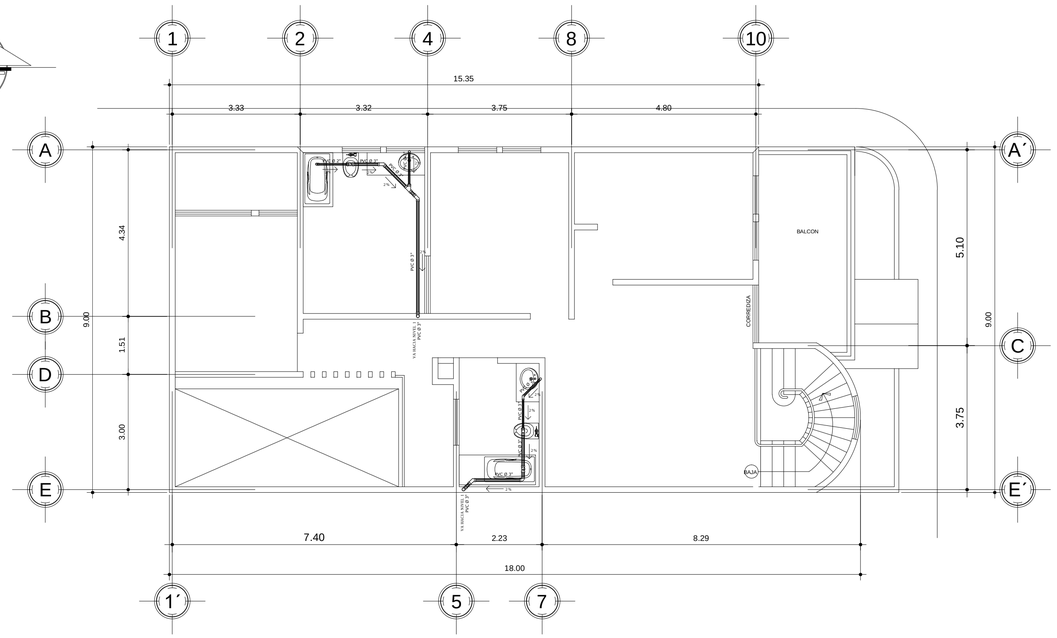

PLANTA DE INST. SANITARIA NIVEL 2

VIVIENDA UNIFAMILIAR 2 NIVELES

ESCALA 1: 75

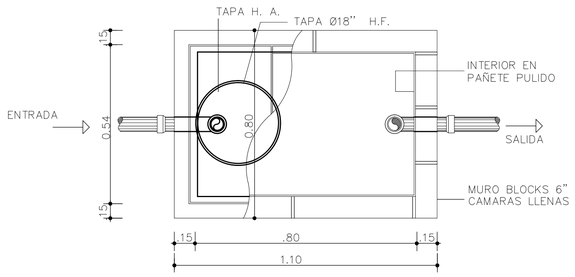

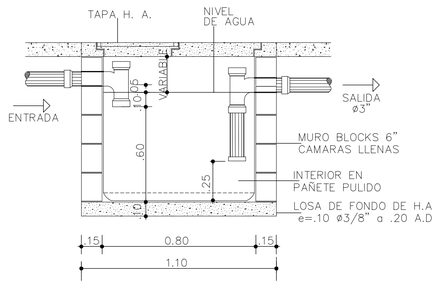

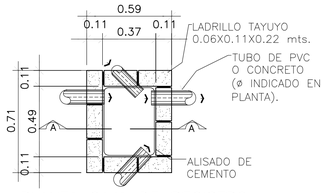

PLANTA CAJA DE REGISTRO

ESCALA 1:25

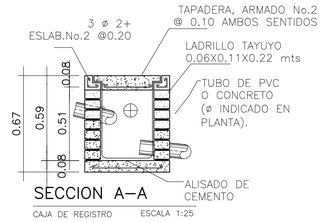

SECCION A–A

CAJA DE REGISTRO ESCALA 1:25

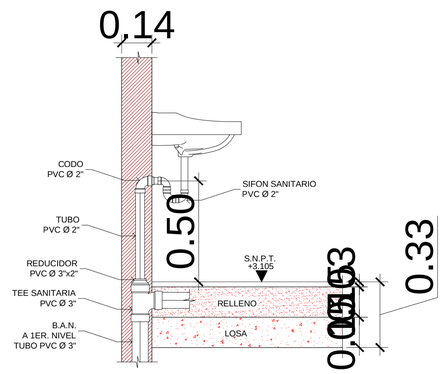

DETALLE
LAVAMANOS Y B.A.N. ESC. 1/12.5

SIMBOLOGIA DE DRENAJES

SÍMBOLO	SIGNIFICADO
R	CAJA DE REGISTRO DE DRENAJE
TG	CAJA ATRAPA GRASA
	DIRECCION DE FLUJO
	TUBO DE DRANAJE AGUAS NEGRAS
	REDUCTOR

SÍMBOLO	SIGNIFICADO
	SIFÓN TERMINAL PERFIL
	TE PERFIL
	TE PLANTA
	TE ELEVACIÓN
	YE
	CODO 90° PERFIL
	CODO 90° ELEVACIÓN
	CODO 45° PERFIL
	CODO 90° BAJA
	BAJADA DE DRENAJE

WD ARQUITECTURA

VIVIENDA UNIFAMILIAR
JUTIAPA, JUTIAPA

UNIDAD: WD ARQUITECTURA

CONTENIDO: PLANO DE INST. SANITARIAS + DETALLES

ESCALA: INDICADA
FECHA: NOVIEMBRE 2021

DISEÑO: WD ARQUITECTURA
DIBUJO: WD ARQUITECTURA
CALCULO: WD ARQUITECTURA

Vo.Bo.

PLANO DE: A E I

HOJA No. 07/09