


## PLANTA DE LOSA PREFABRICADA NIVEL 1

VIVIENDA UNIFAMILIAR 2 NIVELES

ESCALA 1: 75

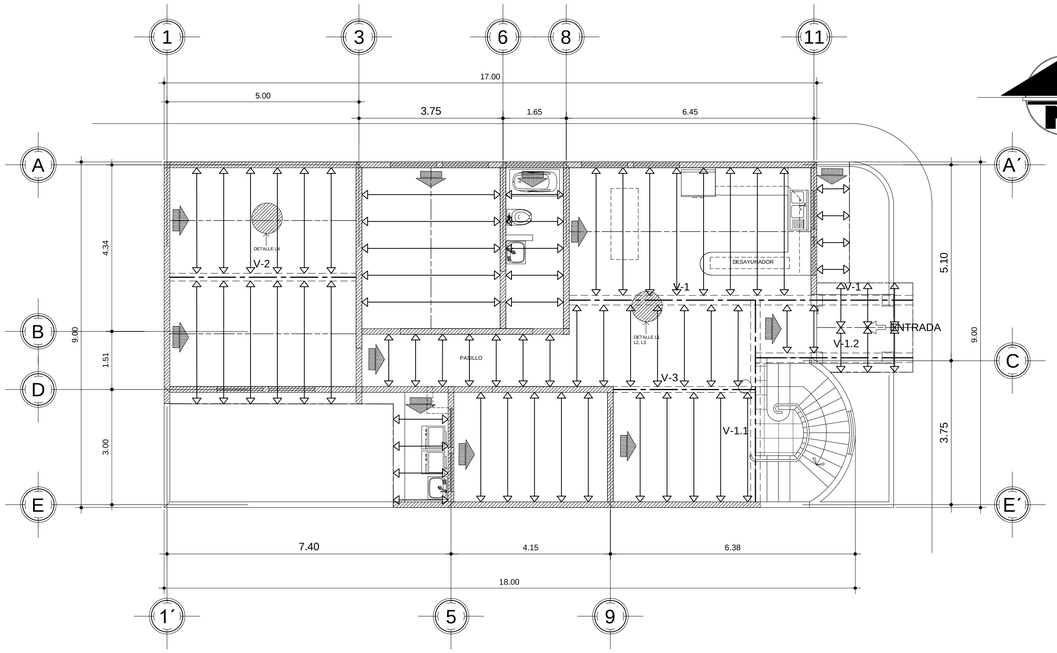


## PLANTA DE LOSA PREFABRICADA NIVEL 2

VIVIENDA UNIFAMILIAR 2 NIVELES

ESCALA 1: 75

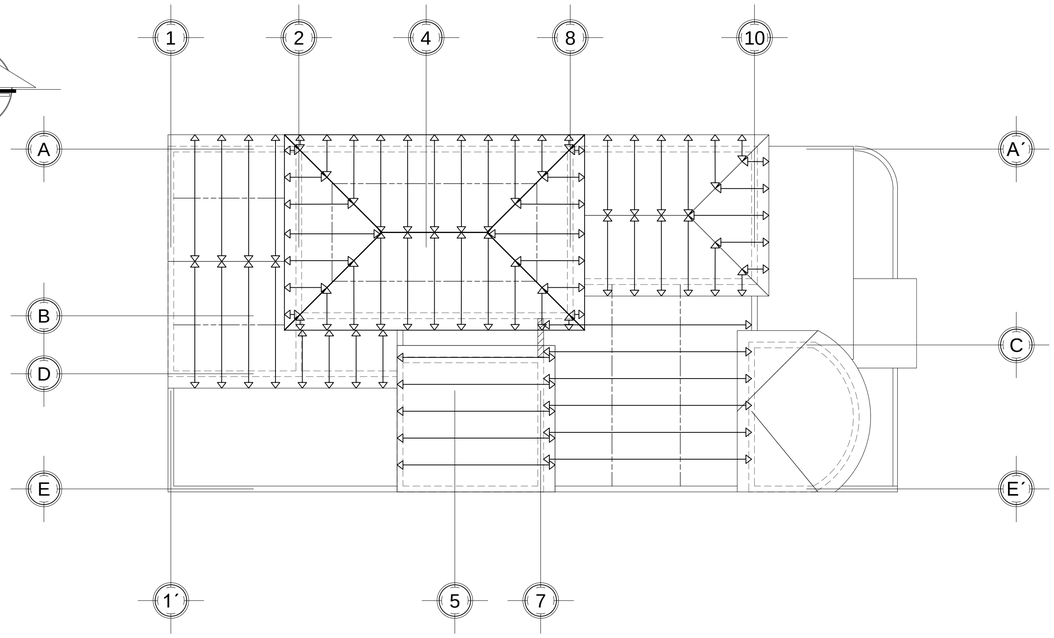


**DETALLE**
DE BLOCK CORTADO EN APOYO
ESCALA 1:10




**DETALLE DE NERVIO RIGIDIZANTE L-4**
DE LOSA PREFABRICADA
ESCALA 1:12.5

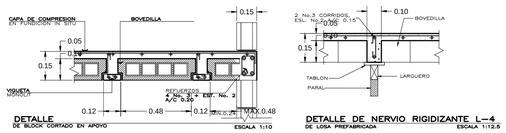


**DETALLE**
INICIO DE MODULACION
ESCALA 1:10




**SECCION TRANSVERSAL**
DE LOSA PREFABRICADA
ESCALA 1:12.5

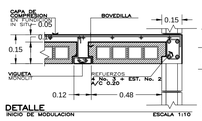


**DETALLE**
APOYO DE VIGUETAS
ESCALA 1:10

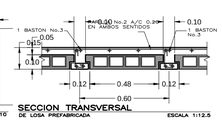


## DETALLE L-3

APOYO DE VIGUETAS
A VIGA INDICADA

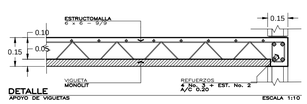ESCALA 1/20

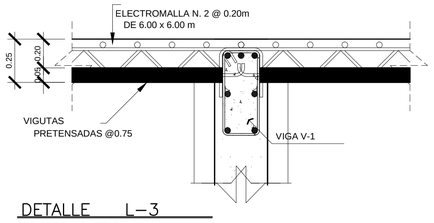


**DETALLE**
REFUERZO PARA MURO SIN CONTINUIDAD

ESC 1:10




ISOMETRICO DE LOSA PREFABRICADA

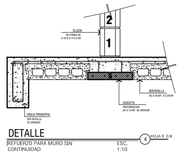SIN ESCALA



Fabricada acorde al proyecto segun especificaciones de la empresa proveedora.

La armadura para vigueta esta formada por varillas longitudinales y diagonales de hierro grado 70 (4,922 kg /cm²) electrosoldadas a máquina entre sí. Se fabrican en largos acordes a cada proyecto.
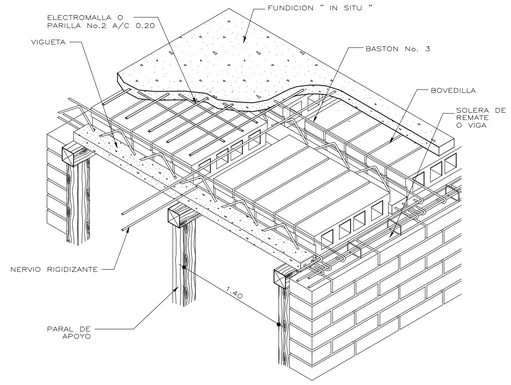
## DETALLE DE VIGUETA

SIN ESCALA

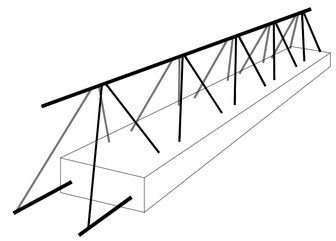


## DETALLE DE ARMADO DE LOSA INCLINADA

LOSA PREFABRICADA

SIN ESCALA

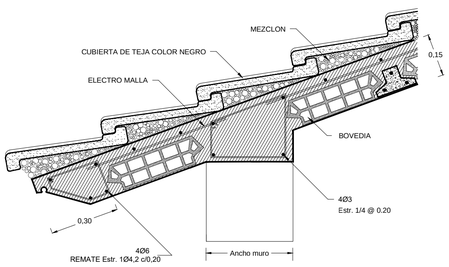


ESTRIBO No. 2 1 @ 0.05 + 0.80 M @ 0.10
RESTO @ 0.15 EN AMBOS EXTREMOS

**SECCION VIGA V-1, V-1.1, V-1.2 V-2**
ESCALA 1:10




ESTRIBO No. 2 1 @ 0.05 + 0.80 M @ 0.10
RESTO @ 0.15 EN AMBOS EXTREMOS

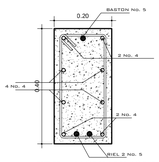**SECCION VIGA V-3**
ESCALA 1:10

## SIMBOLOGIA

| | |
|---|---|
| | INDICA VIGUETAS PRETENSADA |
| | INDICA RIGIDIZANTE |
| | INDICA VIGA DE CONCRETO |
| | INDICA SOLERA DE CORONA O FINAL |
| | INDICA INICIO DE MODULACION DE VIGUETAS |
| | INDICA DETALLE |

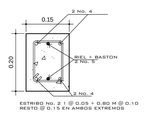WD ARQUITECTURA

VIVIENDA UNIFAMILIAR
JUTIAPA, JUTIAPA

UNIDAD:
WD ARQUITECTURA

CONTENIDO:
PLANO DE LOSA + DETALLES

ESCALA:
INDICADA

FECHA:
NOVIEMBRE 2021

DISEÑO:
WD ARQUITECTURA

DIBUJO:
WD ARQUITECTURA

CALCULO:
WD ARQUITECTURA

Vo.Bo.

PLANO DE:
A E I

HOJA No.
05/09